


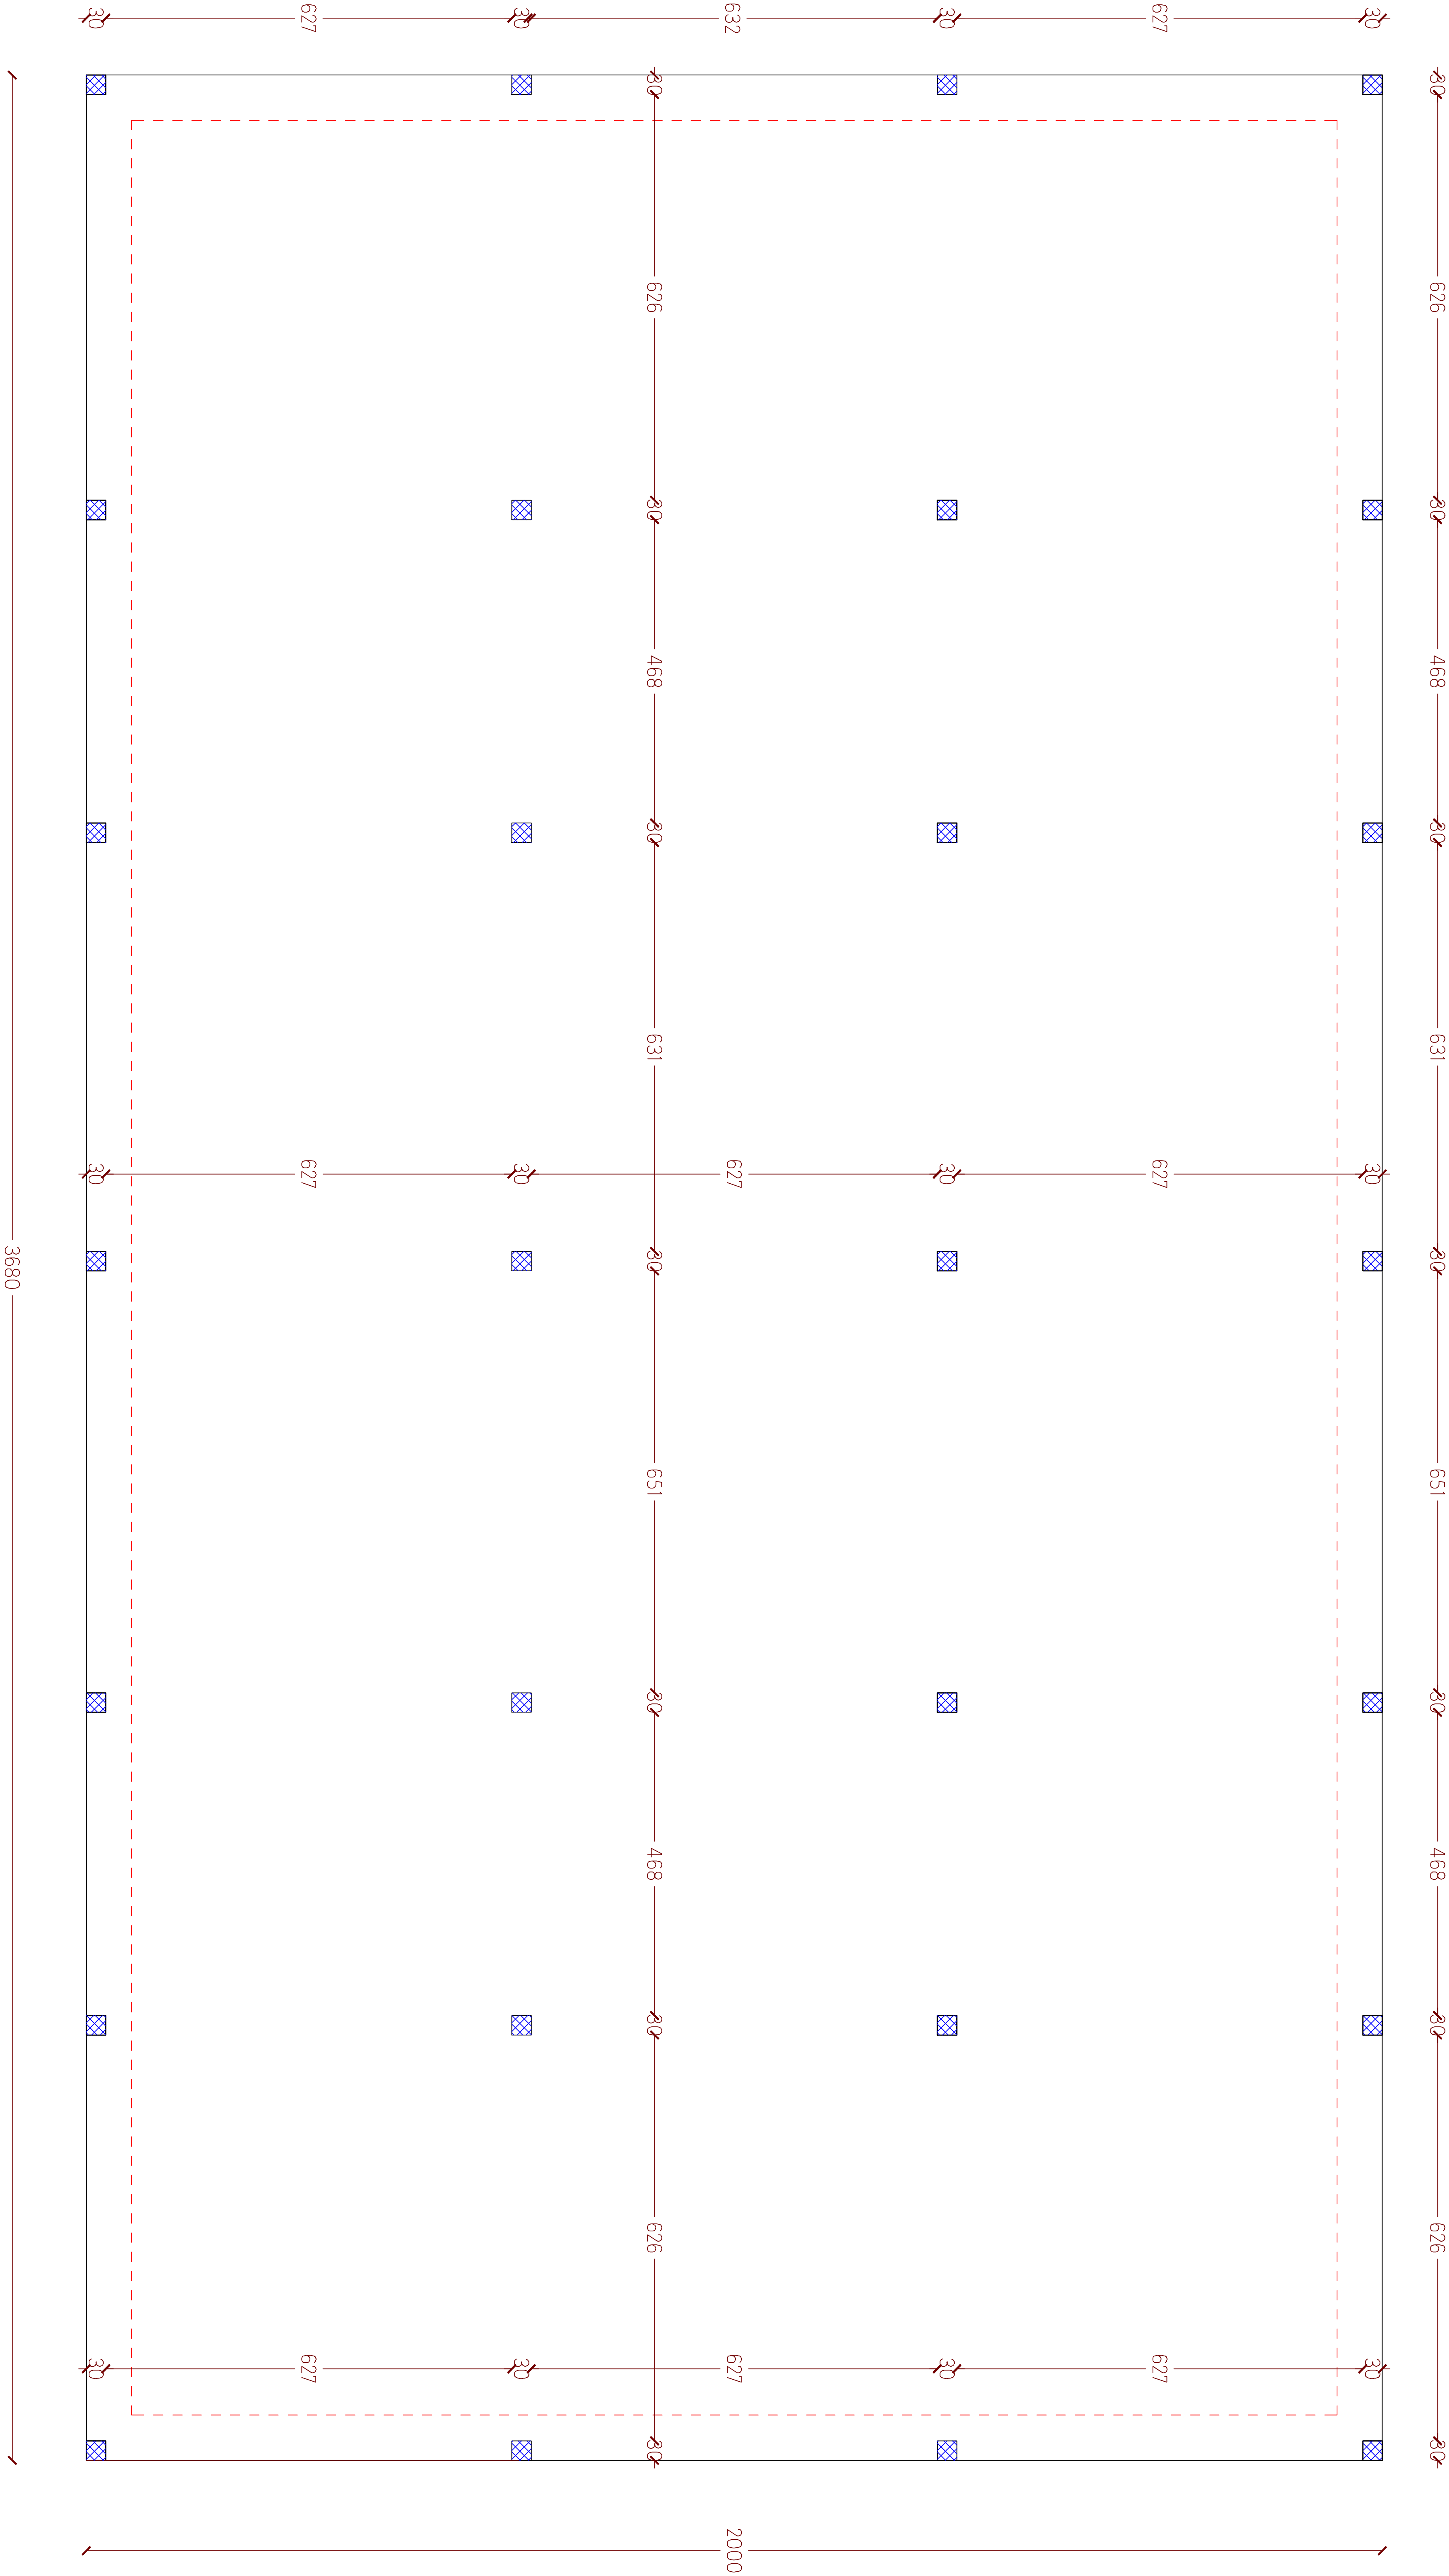

Shtresa e mbështjelljes së betonit						
Për themele dhe mure mbrojtëse Cnom> 50mm						
Për traje Cnom> 30mm						
Për shtylla Cnom> 30mm						
Për pllaka Cnom> 30mm						
Materialët						
Betoni- shtyllat	C30/37					
Betoni- Trajet dhe pllakat	C25/30					
Armatura	S-500					
Parametrat e projektit						
Nxitimi në sipërfaqen e tokës		ag=0.25				
Klasa e rëndësishë		Klasa II				
Faktori i rëndësishë (γ)		γ=1.0				
Faktori i sjelljes (q)		q=3.12				
Kategoria e tokës		Kategoria B				
Parametrat e spekitrit		S=1.15				
		Tb(S)=0.2				
		Tc(S)=0.5				
		Td(S)=2.0				
Trashësia e pllakes		Hpl=25 cm				
L1 [cm] = 6 Ø		L2 [cm] = 11 Ø				
R1=R3 [cm] = 4 Ø për Ø ≤ 16mm		R2 [cm] = 20 Ø				
= 7 Ø për Ø > 16 mm						
Emri i projektit	OBJEKT AFARIST P+0					
Lloji i projektit	PROJEKTI KRYESOR					
Përmbajtja:						
KALLUPIMI I THEMELIT L-2		736.04 m ²				
		07				
Data	Qershor 2026					
INVESTITORI	TAKE AWAY	Vizatoi:				
		Msc.cand Labeat Shumolli				
		Msc. ing Rinor Morina				
		Përpjesa:				
		1:75				
PROJEKTUESI	L&A Engineering	Lokacioni:	Ferizaj			
		V.V				