


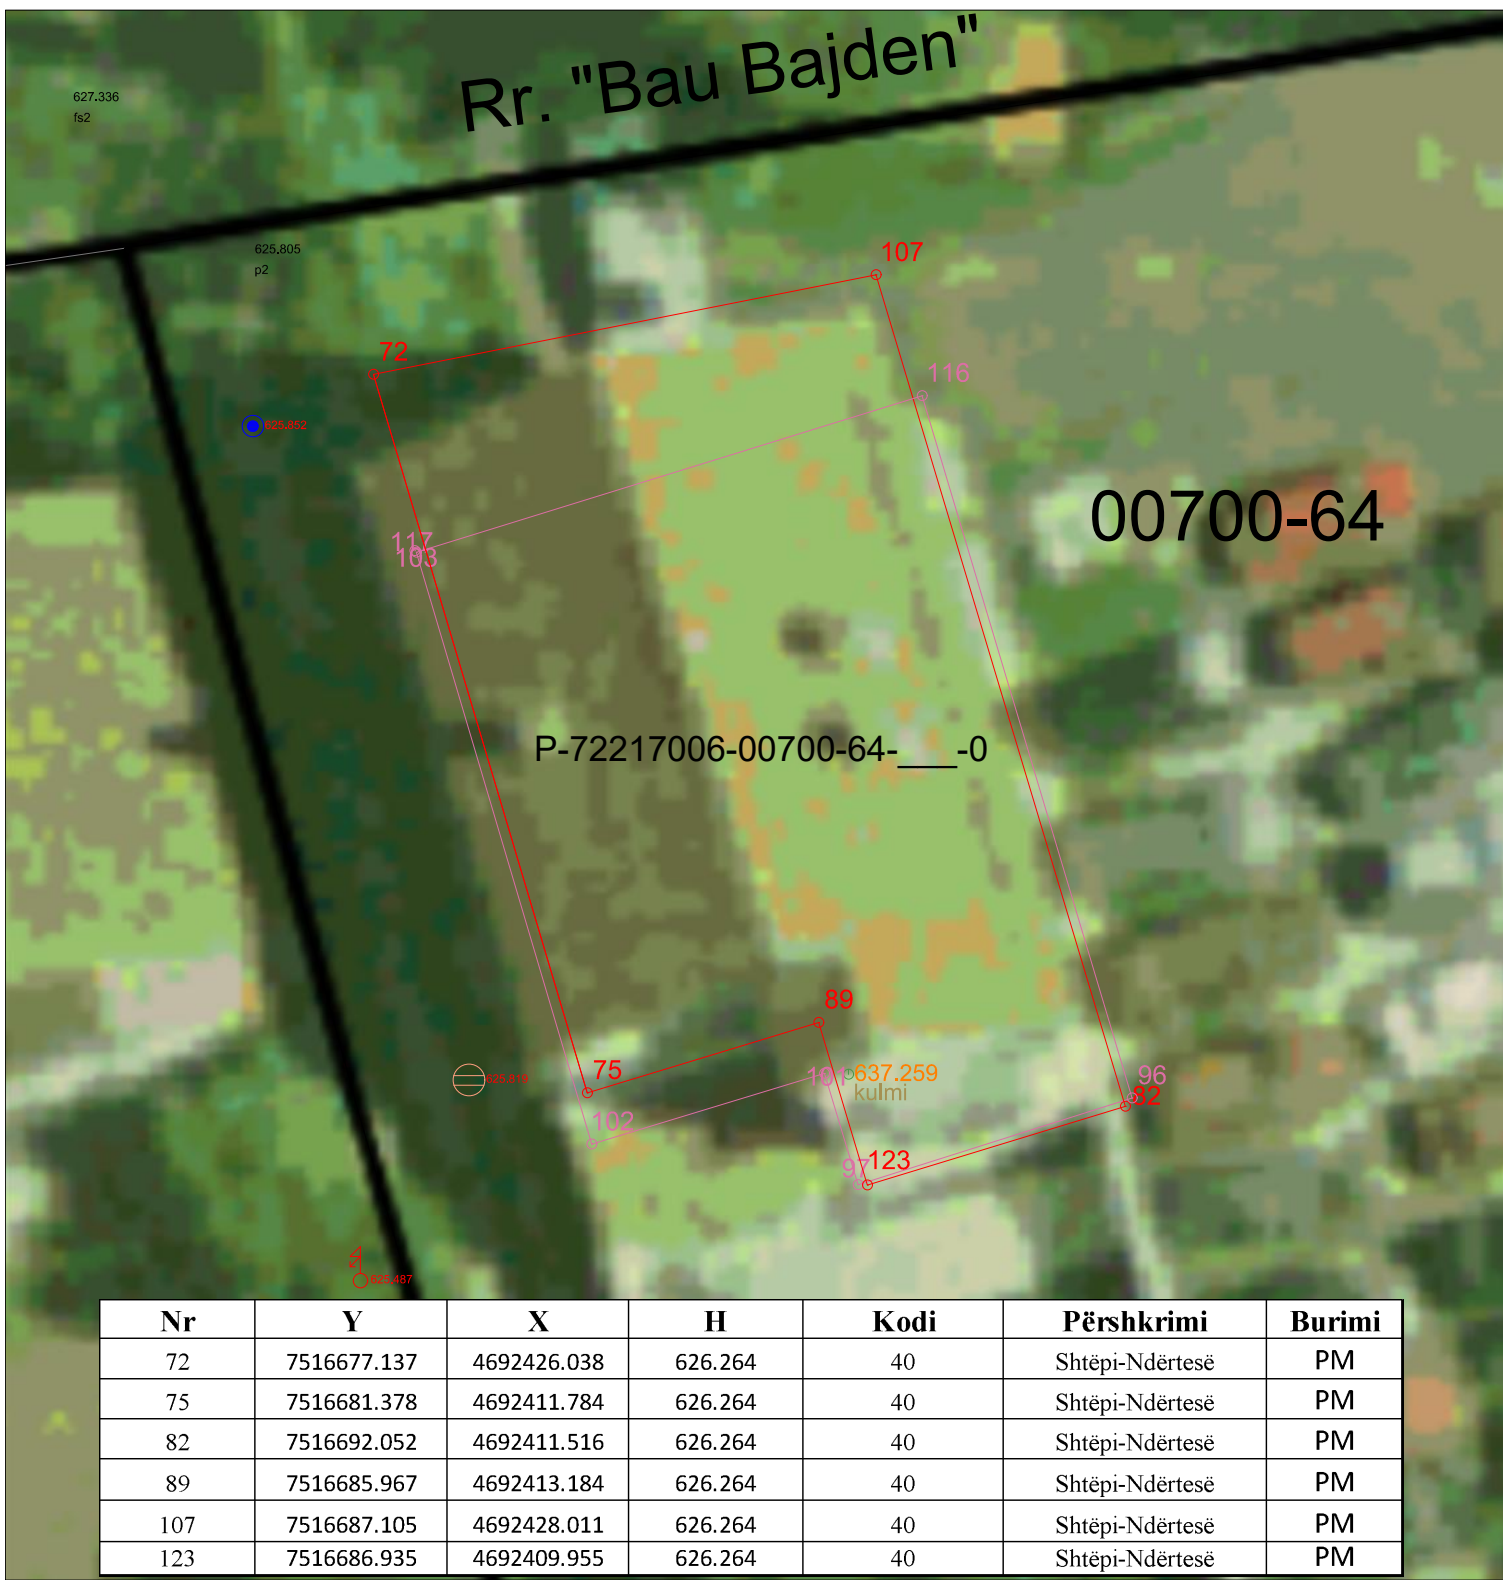

Nr	Y	X	H	Kodi	Përshkrimi	Burimi
72	7516677.137	4692426.038	626.264	40	Shtëpi-Ndërtesë	PM
75	7516681.378	4692411.784	626.264	40	Shtëpi-Ndërtesë	PM
82	7516692.052	4692411.516	626.264	40	Shtëpi-Ndërtesë	PM
89	7516685.967	4692413.184	626.264	40	Shtëpi-Ndërtesë	PM
107	7516687.105	4692428.011	626.264	40	Shtëpi-Ndërtesë	PM
123	7516686.935	4692409.955	626.264	40	Shtëpi-Ndërtesë	PM



Republika e Kosovës
Qeveria - Vlada



Ministria e Mjedisit dhe Planifikimit Hapësinor / Ministarstv Sredine i Prstrng Planiranja
AGJENCIA KADASTRALE E KOSOVËS/ KATASTARSKA AGENCIJA KOSOVA

Situacioni i terrenit

Orto 2004

Zyra kadastrale kmunale / pštinska katastarska kancelarija: Ferizaj

Zona kadastrale / Katastarska zona: Bibaj

Nr. i njësisë kadastrale / Br. katastarske jedinice : 00700-64

Numri i lëndës / Broj predmeta: _____

Shkalla e zvoglimit / Razmera plana 1: 150

Lista e koordinatave të pikave të matura:

Nr	Y	X	H	DSC
118	7516685.600	4692378.988	627.578	fs1
119	7516670.969	4692431.366	627.336	fs2
100	7516686.557	4692412.155	637.259	kulmi
71	7516674.743	4692425.007	625.852	kyqjeUj
120	7516696.920	4692353.097	625.700	p1
121	7516674.570	4692428.347	625.805	p2
122	7516722.548	4692439.805	626.725	p3
72	7516677.137	4692426.038	626.264	perdhese
75	7516681.378	4692411.784	626.264	perdhese
82	7516692.052	4692411.516	626.264	perdhese
89	7516685.967	4692413.184	626.264	perdhese
107	7516687.105	4692428.011	626.264	perdhese
123	7516686.935	4692409.955	626.264	perdhese
70	7516679.028	4692412.039	625.819	pusetFeekkal
8	7516676.879	4692408.060	625.487	shtylElektrike
96	7516692.183	4692411.682	633.750	streha
97	7516686.748	4692409.960	635.102	streha
101	7516686.082	4692412.175	633.750	streha
102	7516681.468	4692410.767	633.606	streha
103	7516677.987	4692422.506	633.703	streha
116	7516688.021	4692425.613	633.738	streha
117	7516677.955	4692422.538	633.690	streha

Shpjegues:

- Kufiri kadastral (nga SIKTK-G)
- Ndërtesa në trajtim për legalizim
- Ndërtesa tjera
- Aneks Ndërtimi
- Shtyllë elektrike
- Pusetë e ujësjellësit
- Pusetë e ujërave të zeza
- Strehët
- Kyqje në rrymë
- Pikë e objekteve fqinje
- Rr. Emri i rrugës
- Pikë e rrjetës gjeodezike
- Pikë e strehëve
- Pikë e terasës
- Pikë e objektit
- Pikë e murit
- Pikë e kulmit

Rilevoi / Snimi: LIRIDON SEJDIU

(emri dhe mbiemri i gjedetit/kompanisë/ ime i prezime gedeta/ kompanije)

Nr. i licencës / Br. licence: 140

Data e rilevimit / Datum snimanja: 02.07.2025

Nënshkrimi / Potpis: _____

v.v.