



Republika e Kosovës
Republika Kosova-Republic of Kosova
Qeveria -Vlada-Government

Ministria e Mjedisit dhe Planifikimit Hapësinor /Ministarstvo Sredine i Prostornog Planiranja/Ministry of Environment and Spatial Planning
AGJENCIA KADASTRALE E KOSOVËS/ KATASTARSKA AGENCIJA KOSOVA/ KOSOVA CADASTRAL AGENCY

Zyra kadastrale komunale / Opštinska katastarska kancelarija: Ferizaj


Nr. i njësish kadastrale / Br. katastarske jedinice : 00959-13

Zona kadastrale / Katastarska zona: Ferizaj

Numri i lëndës / Broj predmeta: _____

Lloji i njësish kadastrale / Vrsta katastarske jedinice : Parcel

Shkalla e zvoglimit / Razmera plana : 1:500

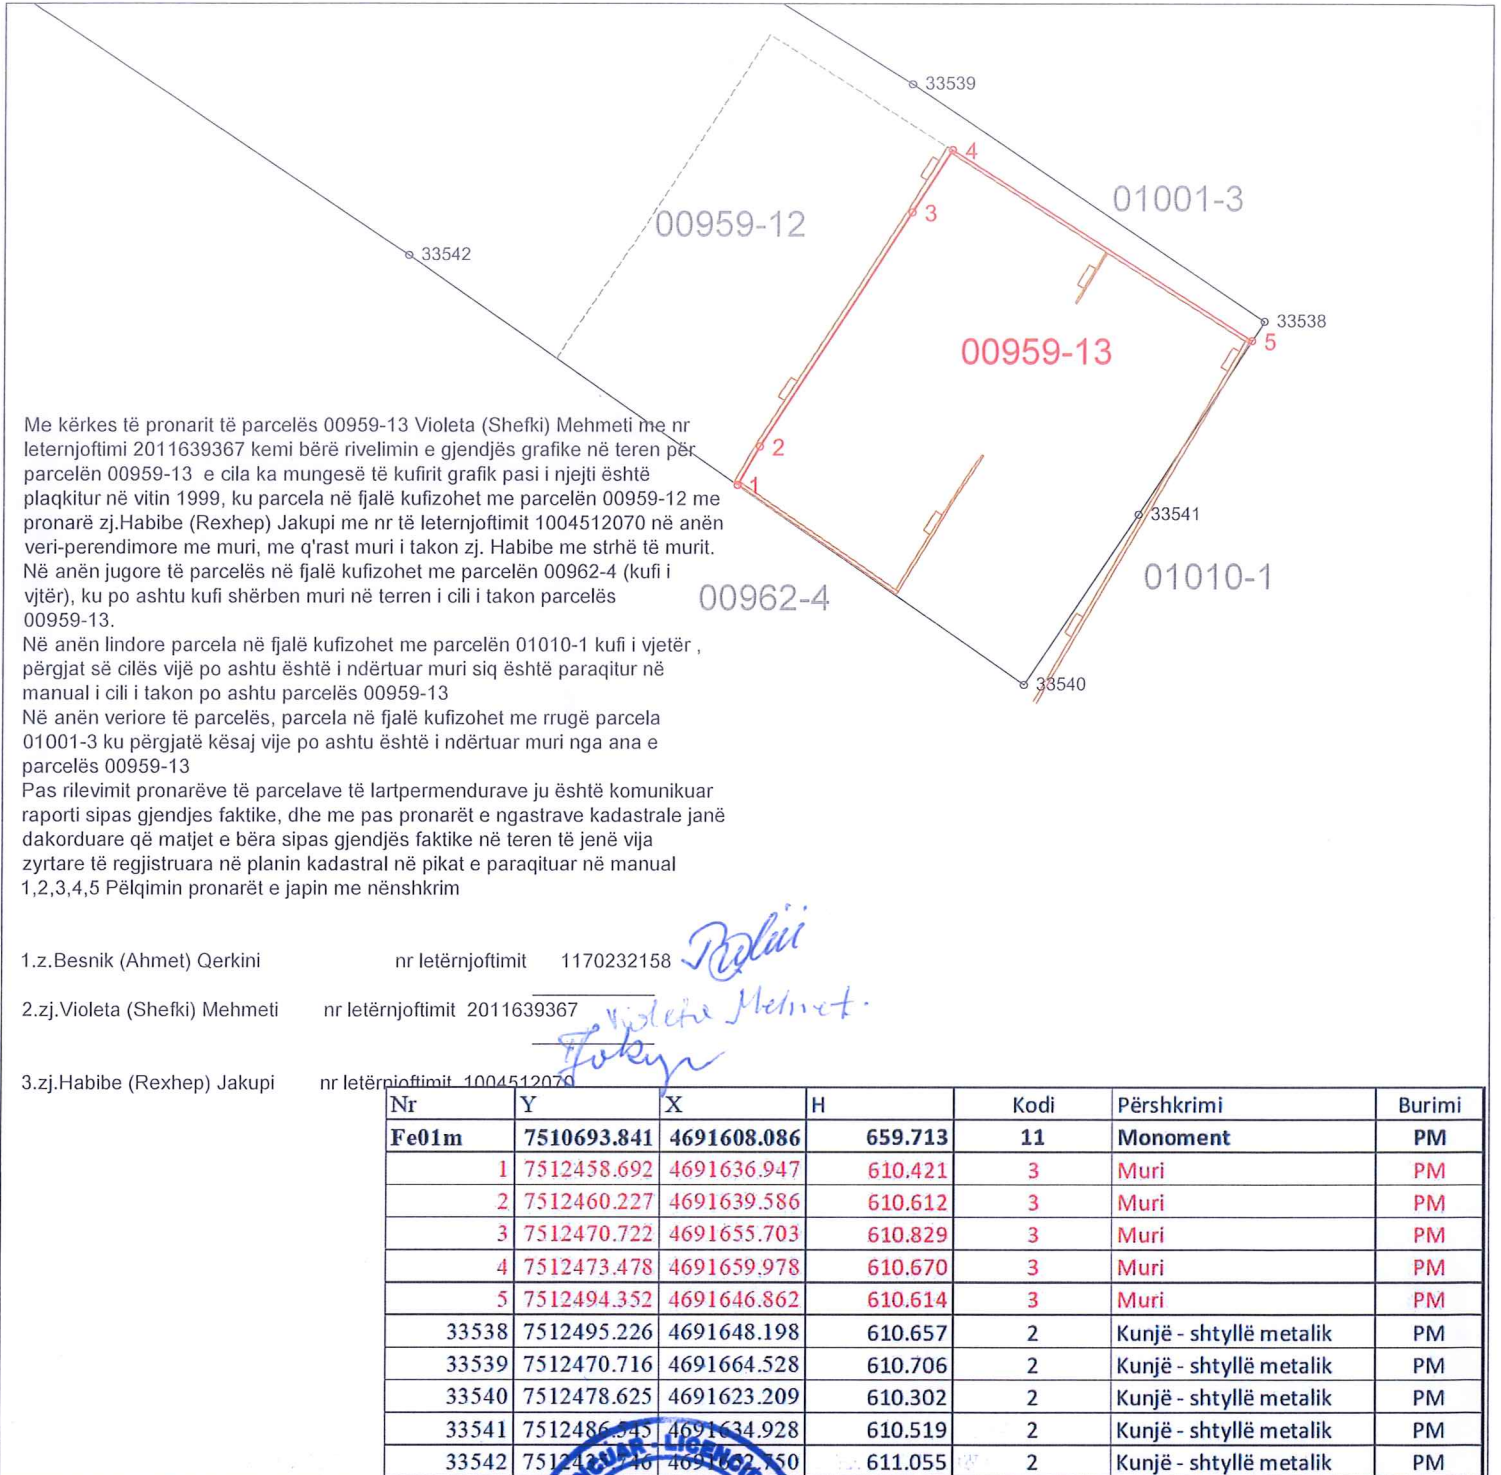

Me kërkesë të pronarit të parcelës 00959-13 Violeta (Shefki) Mehmeti me nr letërnjoftimi 2011639367 kemi bërë rivelimin e gjendjes grafike në teren për parcelën 00959-13 e cila ka mungesë të kufirit grafik pasi i njëjti është plaqitur në vitin 1999, ku parcela në fjalë kufizohet me parcelën 00959-12 me pronarë zj. Habibe (Rexhep) Jakupi me nr të letërnjoftimit 1004512070 në anën veri-perendimore me muri, me q'rast muri i takon zj. Habibe me strhë të murit. Në anën jugore të parcelës në fjalë kufizohet me parcelën 00962-4 (kufi i vjtër), ku po ashtu kufi shërben muri në terren i cili i takon parcelës 00959-13.

Në anën lindore parcela në fjalë kufizohet me parcelën 01010-1 kufi i vjetër, përgjatë së cilës vijë po ashtu është i ndërtuar muri siq është paraqitur në manual i cili i takon po ashtu parcelës 00959-13

Në anën veriore të parcelës, parcela në fjalë kufizohet me rrugë parcela 01001-3 ku përgjatë kësaj vije po ashtu është i ndërtuar muri nga ana e parcelës 00959-13

Pas rievimit pronarëve të parcelave të lartpërmendurave ju është komunikuar raporti sipas gjendjes faktike, dhe me pas pronarët e ngastrave kadastrale janë dakorduar që matjet e bëra sipas gjendjes faktike në teren të jenë vija zyrtare të regjistruara në planin kadastral në pikat e paraqitura në manual 1,2,3,4,5 Pëlqimin pronarët e japin me nënshkrim

1.z.Besnik (Ahmet) Qerkini nr letërnjoftimit 1170232158

2.zj.Violeta (Shefki) Mehmeti nr letërnjoftimit 2011639367

3.zj.Habibe (Rexhep) Jakupi nr letërnjoftimit 1004512070

Nr	Y	X	H	Kodi	Përshkrimi	Burimi
Fe01m	7510693.841	4691608.086	659.713	11	Monoment	PM
1	7512458.692	4691636.947	610.421	3	Muri	PM
2	7512460.227	4691639.586	610.612	3	Muri	PM
3	7512470.722	4691655.703	610.829	3	Muri	PM
4	7512473.478	4691659.978	610.670	3	Muri	PM
5	7512494.352	4691646.862	610.614	3	Muri	PM
33538	7512495.226	4691648.198	610.657	2	Kunjë - shtyllë metalik	PM
33539	7512470.716	4691664.528	610.706	2	Kunjë - shtyllë metalik	PM
33540	7512478.625	4691623.209	610.302	2	Kunjë - shtyllë metalik	PM
33541	7512486.545	4691634.928	610.519	2	Kunjë - shtyllë metalik	PM
33542	7512422.416	4691662.750	611.055	2	Kunjë - shtyllë metalik	PM

Rilevoi / Snimio: LIRIDON SEJDIU

(emri dhe mbiemri i gjeodetit/kompanisë/ ime i prezime geodeta/ kompanisë)

Nr. i licencës / Br. licence: 140

Nënshkrimi / Potpis: _____

Data e rievimit / Datum snimnja: 10.08.2024

Aprovoi / Usvojio: _____

(emri dhe mbiemri i përsoneit zyrtar/ ime i prezime sluzbenog lica)

Nënshkrimi / Potpis: _____

Data e aprovimit / Datum usvajanja: _____