


Nr	Y	X	H	Kodi	Përshkrimi	Burimi
7	7512475.777	4691657.641	611.643	40	Shtëpi-Ndërtesë	PM
8	7512478.443	4691655.982	611.643	40	Shtëpi-Ndërtesë	PM
9	7512481.420	4691648.905	611.643	40	Shtëpi-Ndërtesë	PM
14	7512476.094	4691652.372	611.643	40	Shtëpi-Ndërtesë	PM
43	7512470.535	4691641.819	611.643	40	Shtëpi-Ndërtesë	PM
44	7512475.086	4691638.858	611.643	40	Shtëpi-Ndërtesë	PM
46	7512467.752	4691645.310	611.643	40	Shtëpi-Ndërtesë	PM
55	7512471.300	4691643.001	611.643	40	Shtëpi-Ndërtesë	PM



Republika e Kosovës
Qeveria -Vlada
Ministria e Mjedisit dhe Planifikimit Hapësinor /Ministarstv Sredine i Prstrng Planiranja
AGJENCIA KADASTRALE E KOSOVËS/ KATASTARSKA AGENCIJA KOSOVA

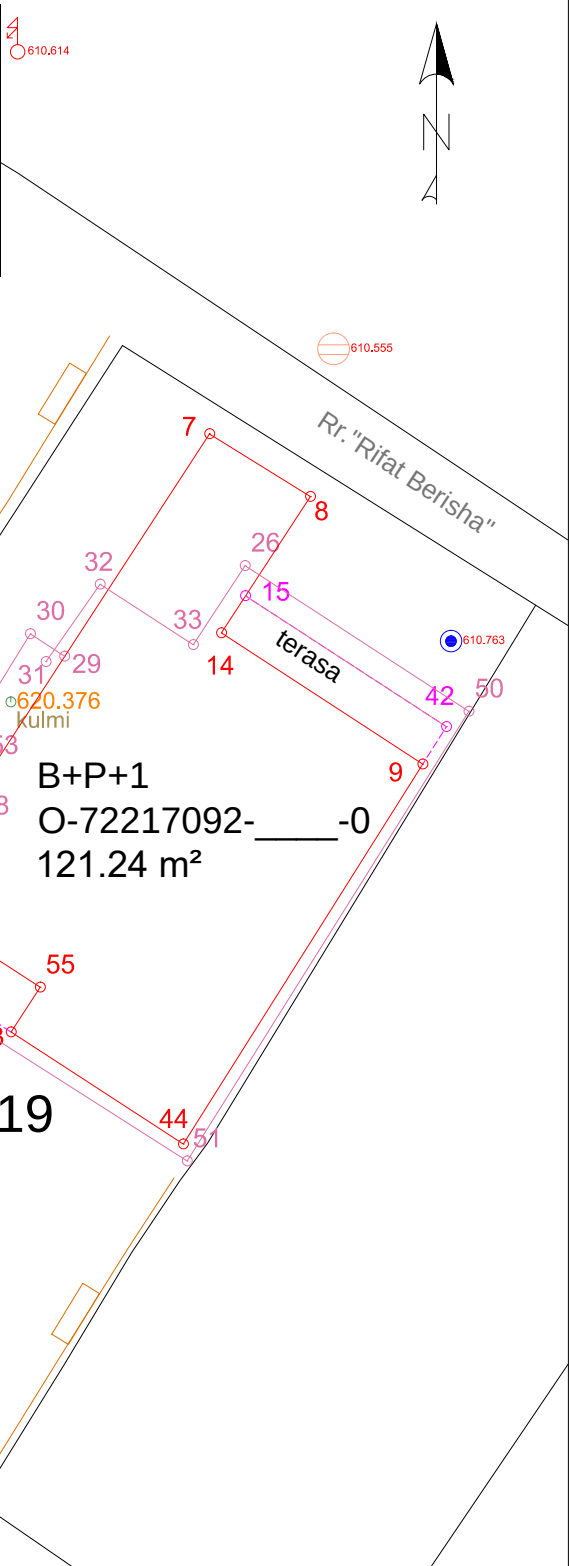

Situacioni i terrenit

Zyra kadastrale kmunale / pštinska katastarska kancelarija: Ferizaj
Zona kadastrale / Katastarska zona: Ferizaj
Nr. i njësisë kadastrale / Br. katastarske jedinice : 00959-19
Numri i lëndës / Broj predmeta: _____
Shkalla e zvoglimit / Razmera plana 1: 200

Lista e koordinatave të pikave të matura:

Nr	Y	X	H	DSC
7	7512475.777	4691657.641	611.643	garazha
8	7512478.443	4691655.982	611.643	garazha
34	7512470.523	4691650.550	620.376	kulmi
60	7512482.163	4691652.152	610.763	kyqje_uji
15	7512476.732	4691653.353	611.643	perdhesa_terasa
17	7512466.984	4691644.130	611.643	perdhesa_terasa
42	7512482.045	4691649.896	611.643	perdhesa_terasa
9	7512481.420	4691648.905	611.643	perdhese
14	7512476.094	4691652.372	611.643	perdhese
43	7512470.535	4691641.819	611.643	perdhese
44	7512475.086	4691638.858	611.643	perdhese
46	7512467.752	4691645.310	611.643	perdhese
55	7512471.300	4691643.001	611.643	perdhese
4	7512479.057	4691659.880	610.555	pusetfeekkal
1	7512470.702	4691667.743	610.614	shtyllElektrike
26	7512476.716	4691654.156	618.000	streha
27	7512466.646	4691643.851	617.341	streha
28	7512469.739	4691648.362	617.272	streha
29	7512471.949	4691651.760	618.975	streha
30	7512471.039	4691652.352	618.958	streha
31	7512471.455	4691651.614	617.434	streha
32	7512472.883	4691653.664	617.291	streha
33	7512475.351	4691652.058	619.036	streha
50	7512482.641	4691650.301	617.247	streha
51	7512475.185	4691638.405	617.223	streha
53	7512469.806	4691648.802	617.239	streha
54	7512468.910	4691648.891	618.931	streha

Shpjegues:

- Kufiri kadastral (nga SIKTK-G)
- Ndërtesa në trajtim për legalizim
- Ndërtesa tjera
- Aneks Ndërtimi
- Shtyllë elektrike
- Pusetë e ujësjellësit
- Pusetë e ujërave të zeza
- Strehët
- Kyqje në rrymë

- Pikë e objekteve fqinje
- Emri i rrugës
- Pikë e rrjetës gjeodezike
- Pikë e strehëve
- Pikë e terasës
- Pikë e objektit
- Pikë e murit
- Pikë e kulmit

Rilevoi / Snimi: LIRIDON SEJDIU

(emri dhe mbiemri i gjedetit/kompanisë/ ime i prezime gedeta/ kompanije)


Nr. i licencës / Br. licence: 140

Data e rilevimit / Datum snimanja: 31.10.2025

Nënshkrimi / Potpis: _____


v.v.

Nr	Y	X	H	Kodi	Përshkrimi	Burimi
7	7512475.777	4691657.641	611.643	40	Shtëpi-Ndërtesë	PM
8	7512478.443	4691655.982	611.643	40	Shtëpi-Ndërtesë	PM
9	7512481.420	4691648.905	611.643	40	Shtëpi-Ndërtesë	PM
14	7512476.094	4691652.372	611.643	40	Shtëpi-Ndërtesë	PM
43	7512470.535	4691641.819	611.643	40	Shtëpi-Ndërtesë	PM
44	7512475.086	4691638.858	611.643	40	Shtëpi-Ndërtesë	PM
46	7512467.752	4691645.310	611.643	40	Shtëpi-Ndërtesë	PM
55	7512471.300	4691643.001	611.643	40	Shtëpi-Ndërtesë	PM

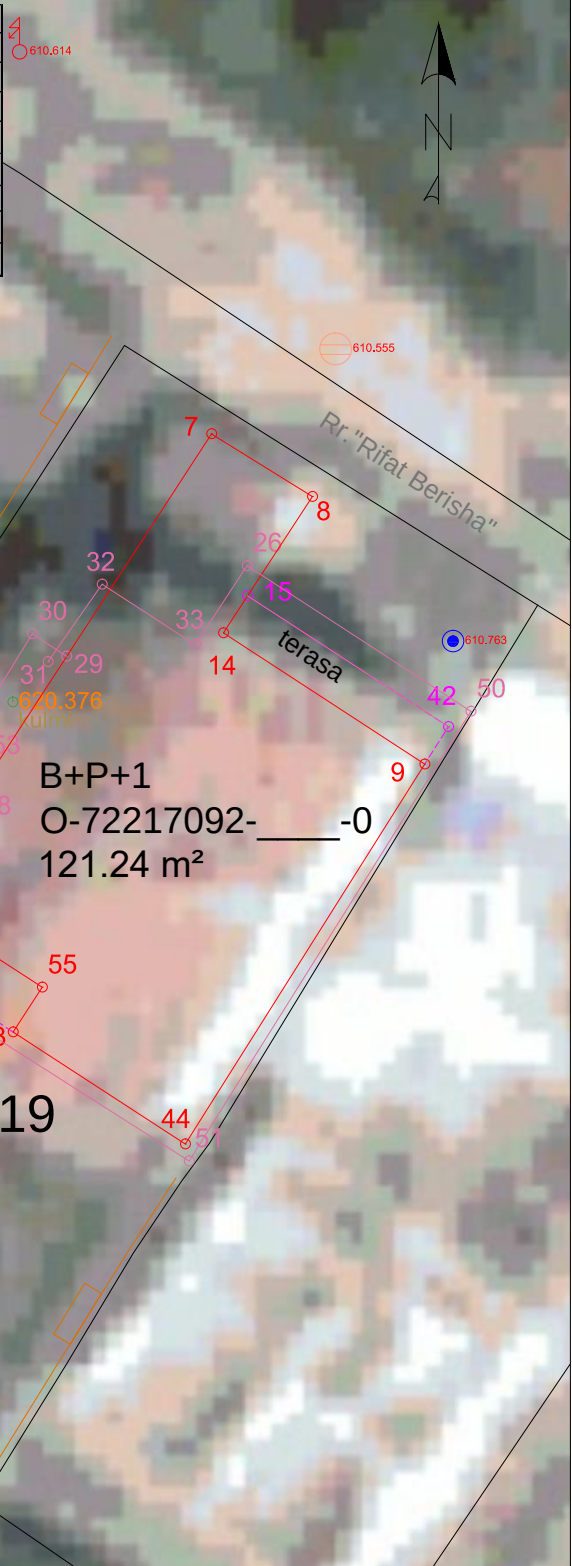

Republika e Kosovës Qeveria -Vlada

Ministria e Mjedisit dhe Planifikimit Hapësinor /Ministarstv Sredine i Prstrng Planiranja
AGJENCIA KADASTRALE E KOSOVËS/ KATASTARSKA AGENCIJA KOSOVA

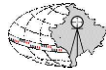

Situacioni i terrenit

Orto 2001

Zyra kadastrale kmunale / pštinska katastarska kancelarija: Ferizaj

Zona kadastrale / Katastarska zona: Ferizaj

Nr. i njësisë kadastrale / Br. katastarske jedinice : 00959-19

Numri i lëndës / Broj predmeta: _____

Shkalla e zvoglimit / Razmera plana 1: 200

Lista e koordinatave të pikave të matura:

Nr	Y	X	H	DSC
7	7512475.777	4691657.641	611.643	garazha
8	7512478.443	4691655.982	611.643	garazha
34	7512470.523	4691650.550	620.376	kulmi
60	7512482.163	4691652.152	610.763	kyqje_uji
15	7512476.732	4691653.353	611.643	perdhesa_terasa
17	7512466.984	4691644.130	611.643	perdhesa_terasa
42	7512482.045	4691649.896	611.643	perdhesa_terasa
9	7512481.420	4691648.905	611.643	perdhese
14	7512476.094	4691652.372	611.643	perdhese
43	7512470.535	4691641.819	611.643	perdhese
44	7512475.086	4691638.858	611.643	perdhese
46	7512467.752	4691645.310	611.643	perdhese
55	7512471.300	4691643.001	611.643	perdhese
4	7512479.057	4691659.880	610.555	pusetfeekkal
1	7512470.702	4691667.743	610.614	shtylElektrike
26	7512476.716	4691654.156	618.000	streha
27	7512466.646	4691643.851	617.341	streha
28	7512469.739	4691648.362	617.272	streha
29	7512471.949	4691651.760	618.975	streha
30	7512471.039	4691652.352	618.958	streha
31	7512471.455	4691651.614	617.434	streha
32	7512472.883	4691653.664	617.291	streha
33	7512475.351	4691652.058	619.036	streha
50	7512482.641	4691650.301	617.247	streha
51	7512475.185	4691638.405	617.223	streha
53	7512469.806	4691648.802	617.239	streha
54	7512468.910	4691648.891	618.931	streha

Shpjegues:

- Kufiri kadastral (nga SIKTK-G)
- Ndërtesa në trajtim për legalizim
- Ndërtesa tjera
- Aneks Ndërtimi
- Shtyllë elektrike
- Pusetë e ujësjellësit
- Pusetë e ujërave të zeza
- Strehët
- Kyqje në rrymë

- Pikë e objekteve fqinje
- Emri i rrugës
- Pikë e rrjetës gjeodezike
- Pikë e strehëve
- Pikë e terasës
- Pikë e objektit
- Pikë e murit
- Pikë e kulmit

Rilevoi / Snimi: LIRIDON SEJDIU

(emri dhe mbiemri i gjedetit/kompanisë/ ime i prezime gedeta/ kompanije)


Nr. i licencës / Br. licence: 140

Data e rilevimit / Datum snimanja: 31.10.2025

Nënshkrimi / Potpis: _____

V.V.

Nr	Y	X	H	Kodi	Përshkrimi	Burimi
7	7512475.777	4691657.641	611.643	40	Shtëpi-Ndërtesë	PM
8	7512478.443	4691655.982	611.643	40	Shtëpi-Ndërtesë	PM
9	7512481.420	4691648.905	611.643	40	Shtëpi-Ndërtesë	PM
14	7512476.094	4691652.372	611.643	40	Shtëpi-Ndërtesë	PM
43	7512470.535	4691641.819	611.643	40	Shtëpi-Ndërtesë	PM
44	7512475.086	4691638.858	611.643	40	Shtëpi-Ndërtesë	PM
46	7512467.752	4691645.310	611.643	40	Shtëpi-Ndërtesë	PM
55	7512471.300	4691643.001	611.643	40	Shtëpi-Ndërtesë	PM

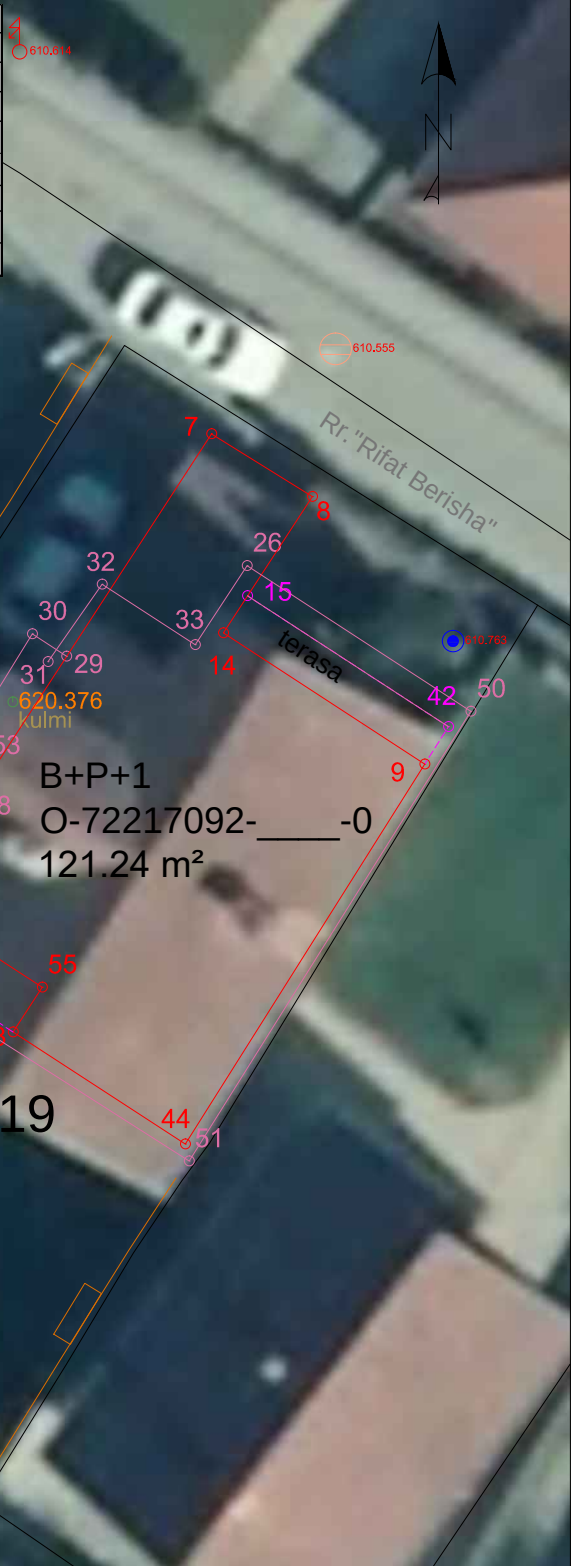

Republika e Kosovës Qeveria - Vlada

Ministria e Mjedisit dhe Planifikimit Hapësinor / Ministarstv Sredine i Prstrng Planiranja
AGJENCIA KADASTRALE E KOSOVËS/ KATASTARSKA AGENCIJA KOSOVA



Situacioni i terrenit

Orto 2018

Zyra kadastrale kmunale / pštinska katastarska kancelarija: Ferizaj

Zona kadastrale / Katastarska zona: Ferizaj

Nr. i njësisë kadastrale / Br. katastarske jedinice : 00959-19

Numri i lëndës / Broj predmeta: _____

Shkalla e zvoglimit / Razmera plana 1: 200

Lista e koordinatave të pikave të matura:

Nr	Y	X	H	DSC
7	7512475.777	4691657.641	611.643	garazha
8	7512478.443	4691655.982	611.643	garazha
34	7512470.523	4691650.550	620.376	kulmi
60	7512482.163	4691652.152	610.763	kyqje_uji
15	7512476.732	4691653.353	611.643	perdhesa_terasa
17	7512466.984	4691644.130	611.643	perdhesa_terasa
42	7512482.045	4691649.896	611.643	perdhesa_terasa
9	7512481.420	4691648.905	611.643	perdhese
14	7512476.094	4691652.372	611.643	perdhese
43	7512470.535	4691641.819	611.643	perdhese
44	7512475.086	4691638.858	611.643	perdhese
46	7512467.752	4691645.310	611.643	perdhese
55	7512471.300	4691643.001	611.643	perdhese
4	7512479.057	4691659.880	610.555	pusetfeekkal
1	7512470.702	4691667.743	610.614	shtylElektrike
26	7512476.716	4691654.156	618.000	streha
27	7512466.646	4691643.851	617.341	streha
28	7512469.739	4691648.362	617.272	streha
29	7512471.949	4691651.760	618.975	streha
30	7512471.039	4691652.352	618.958	streha
31	7512471.455	4691651.614	617.434	streha
32	7512472.883	4691653.664	617.291	streha
33	7512475.351	4691652.058	619.036	streha
50	7512482.641	4691650.301	617.247	streha
51	7512475.185	4691638.405	617.223	streha
53	7512469.806	4691648.802	617.239	streha
54	7512468.910	4691648.891	618.931	streha

Shpjegues:

- Kufiri kadastral (nga SIKTK-G)
- Ndërtesa në trajtim për legalizim
- Ndërtesa tjera
- Aneks Ndërtimi
- Shtyllë elektrike
- Pusetë e ujësjellësit
- Pusetë e ujërave të zeza
- Strehët
- Kyqje në rrymë

- Pikë e objekteve fqinje
- Emri i rrugës
- Pikë e rrjetës gjeodezike
- Pikë e strehëve
- Pikë e terasës
- Pikë e objektit
- Pikë e murit
- Pikë e kulmit

Rilevoi / Snimi: LIRIDON SEJDIU

(emri dhe mbiemri i gjedetit/kompanisë/ ime i prezime gedeta/ kompanije)

Nr. i licencës / Br. licence: 140



Data e rilevimit / Datum snimanja: 31.10.2025

Nënshkrimi / Potpis: _____

V.V.

TË GJITHA

AKTIVE

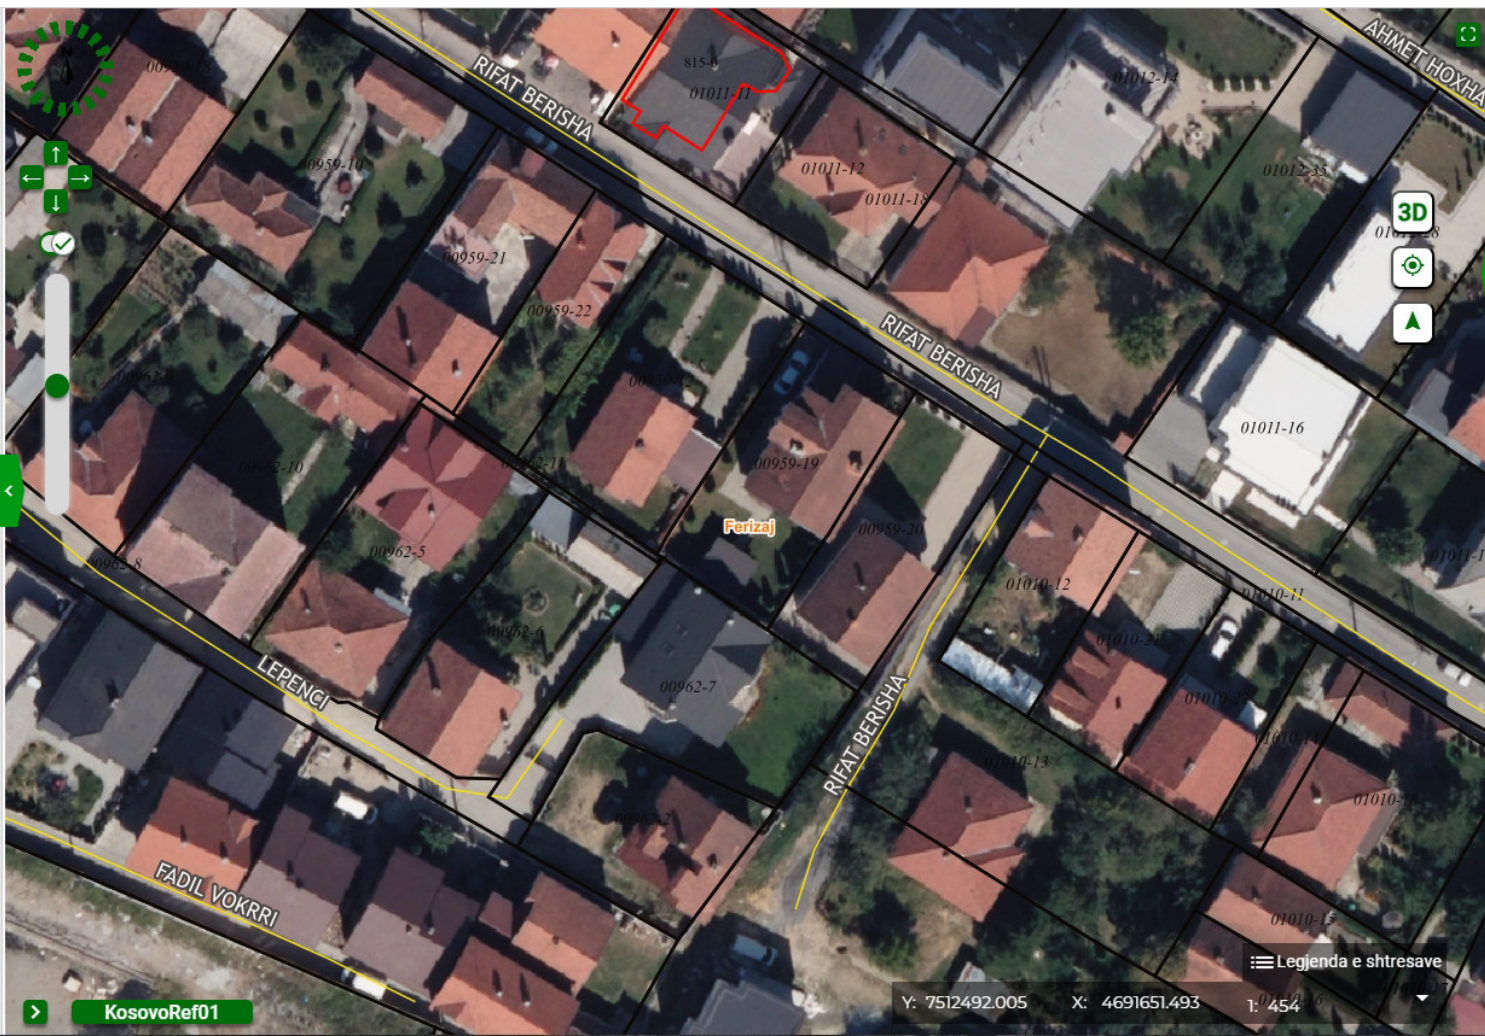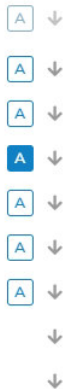☒ Ortofoto 2018 Urban☒ Kufijtë dhe Emrat e Komunave☒ Zona Kadastrale☒ Parcelat☒ Numri i Parcelës☒ Ndërtesat☒ Numri i Ndërtesës☒ Pjesë të ndërtesës☒ Rrugët☒ Emrat e rrugëve

Zona Kadastrale

Ferizaj

ID e Njesisë Kadastrale

00959

Kërko...

ID e Njesisë
Kadastrale

Sipërfaqe

P- 72217092- 00959-10	576.1 m ²	i
P- 72217092- 00959-12	447.4 m ²	i
P- 72217092- 00959-15	211.8 m ²	i
P- 72217092- 00959-16	198.3 m ²	i
P- 72217092- 00959-17	345.4 m ²	i
P- 72217092- 00959-18	345.4 m ²	i
P- 72217092- 00959-19	365.4 m ²	i

Legjenda e shtresave

KosovoRef01

Y: 7512492.005 X: 4691651.493

L: 454

TË GJITHA AKTIVE

Ortofoto

- ✓ Ortofoto 2024 Rurale
- ✓ Ortofoto 2024 Urban
- ✓ Ortofoto 2018 Rurale
- ✓ Ortofoto 2018 Urban
- ✓ Ortofoto 2018 Malore
- ✓ Orthophoto_2015UAV
- ✓ Ortofoto 2012
- ✓ Ortofoto 2009
- ✓ Ortofoto 2004
- ✓ **Ortofoto 2001**

- + Njësit administrative
- + Modeli Dixhital i Terrenit
- + Hartat Topografike
- + Rindërtimi i Infomacioneve Kadastrale
- + Njësit Kadastrale
- + Sistemi i Adresave
- + Rrjeti Rrugor
- + Rrjetat Referente
- + Gjeodetët e Licencuar
- + Policia e Kosovës
- + Posta e Republikës së Kosovës




00959		
Kërko...		
ID e Njësies Kadastrale	Sipërfaqe	
P-72217092-00959-10	576.1 m²	i
P-72217092-00959-12	447.4 m²	i
P-72217092-00959-15	211.8 m²	i
P-72217092-00959-16	198.3 m²	i
P-72217092-00959-17	345.4 m²	i
P-72217092-00959-18	345.4 m²	i
P-72217092-00959-19	365.4 m²	i
P-72217092-00959-20	318.9 m²	i
P-		


KosovoRef01

Y: 7512412.490 X: 4691671.507 1: 448

Legjenda e shtrësive

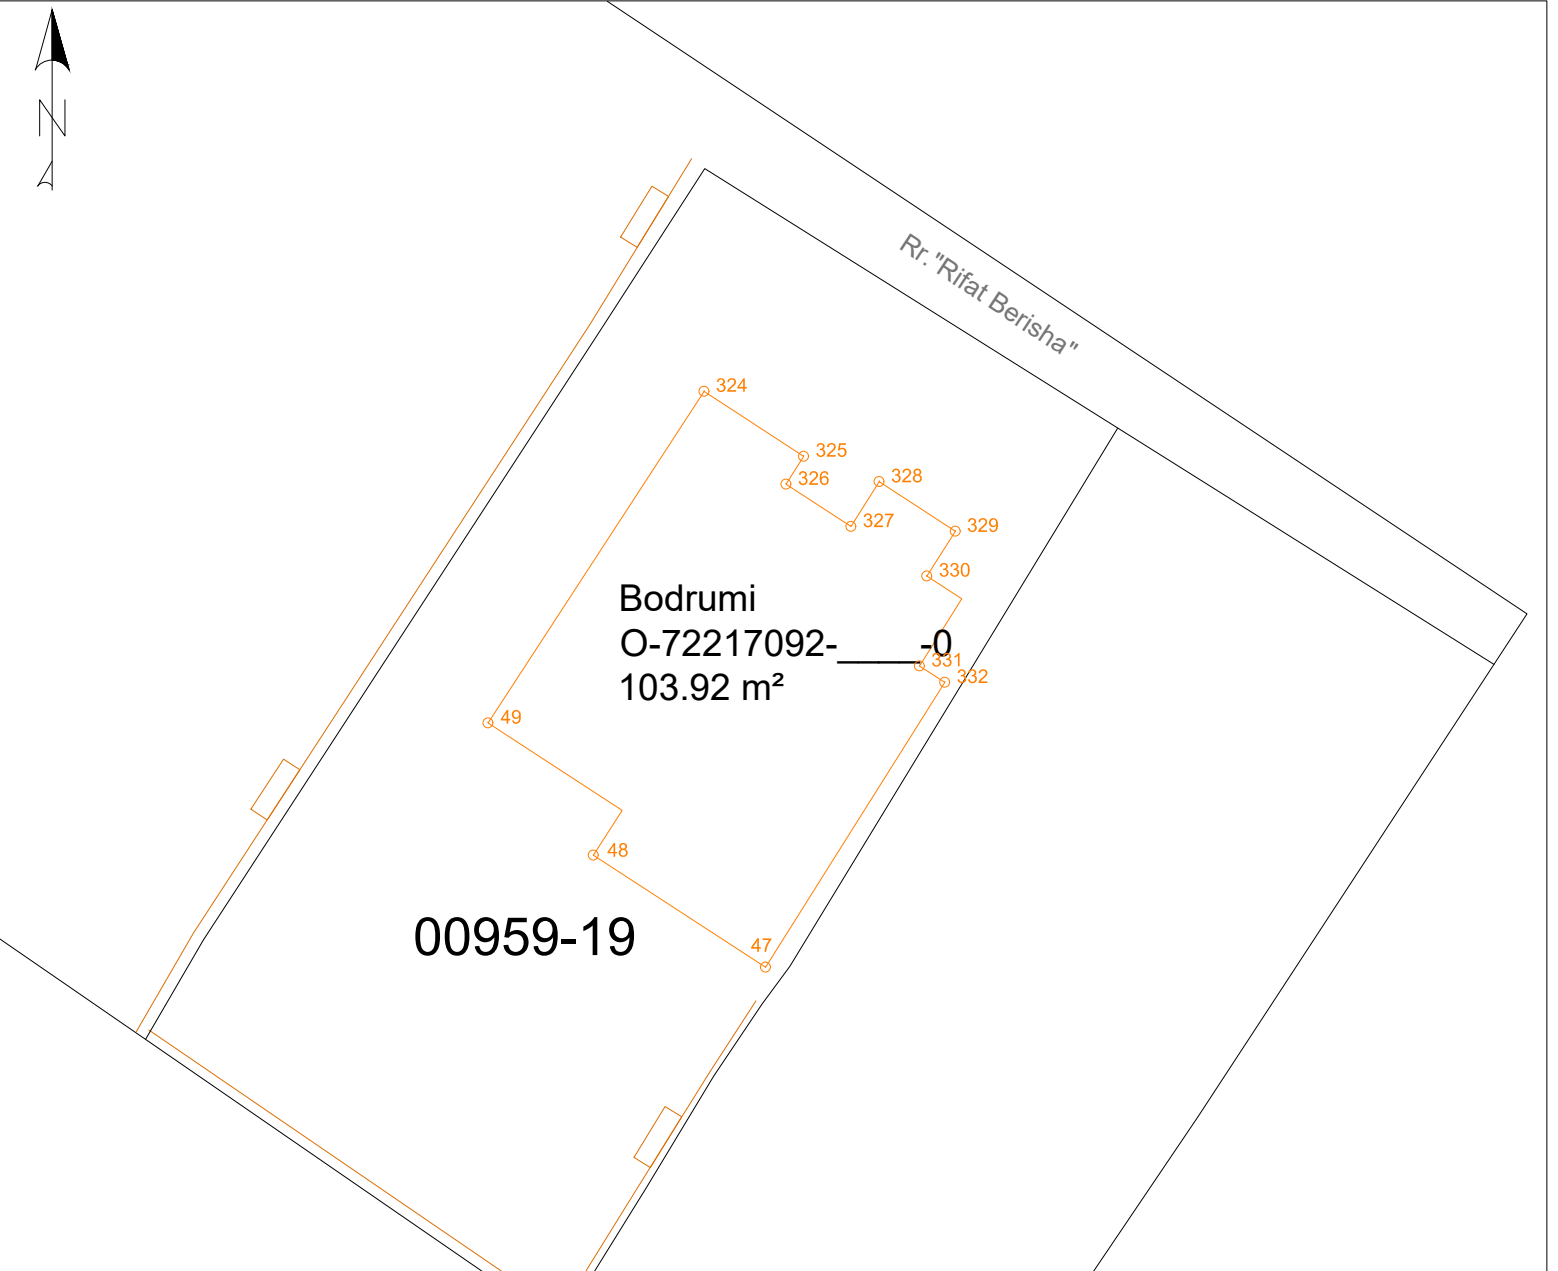

Nr.	Y	X	H	D	Etazhi	Sqarim	Sipërfaqja (m²)
47	7512475.086	4691638.858	103.921	bodrumi	Bodrumi	Bodrumi	103.92
48	7512470.532	4691641.821	103.921	bodrumi			
49	7512467.752	4691645.31	103.921	bodrumi			
324	7512473.462	4691654.084	103.921	bodrumi			
325	7512476.1	4691652.368	103.921	bodrumi			
326	7512475.631	4691651.624	103.921	bodrumi			
327	7512477.347	4691650.507	103.921	bodrumi			
328	7512478.094	4691651.692	103.921	bodrumi			
329	7512480.106	4691650.383	103.921	bodrumi			
330	7512479.359	4691649.198	103.921	bodrumi			
331	7512479.161	4691646.821	103.921	bodrumi			
332	7512479.831	4691646.385	103.921	bodrumi			
						Gjithsej:	

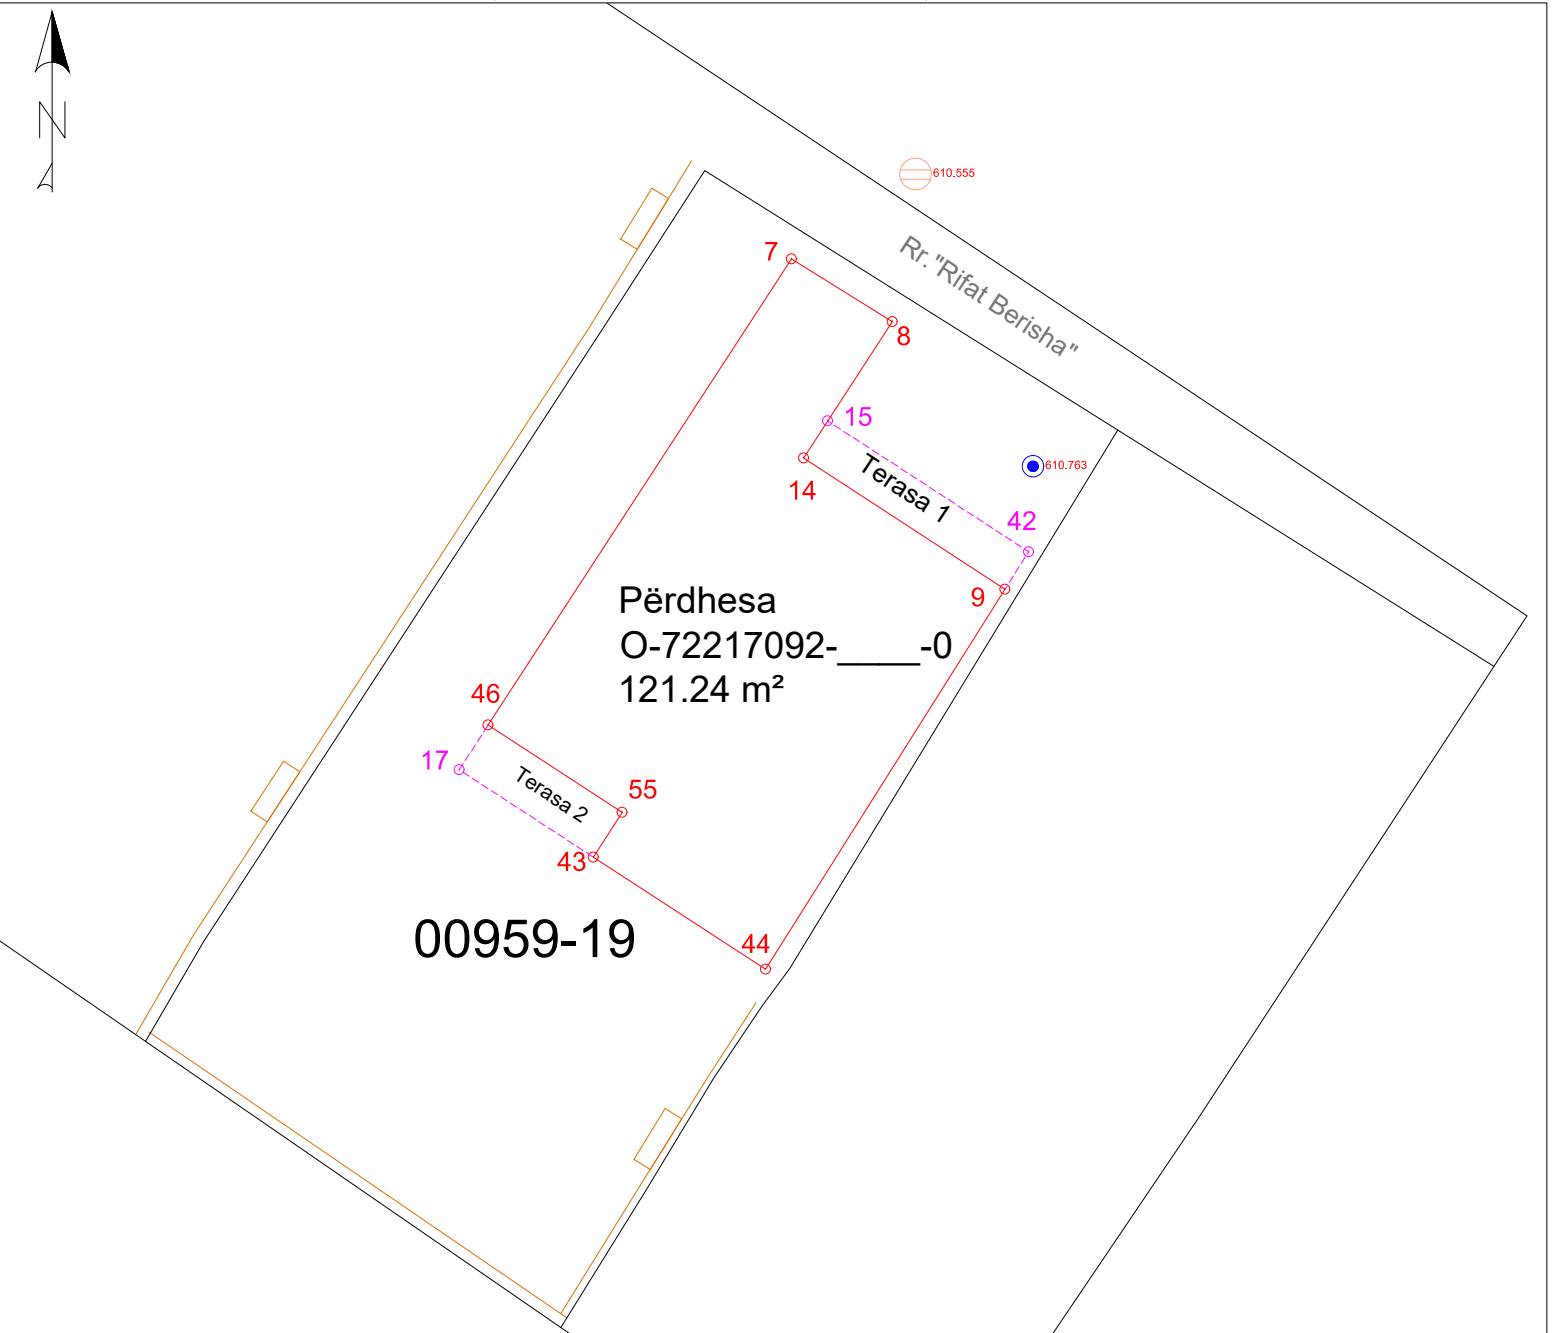

Nr.	Y	X	H	D	Etazhi	Sqarim	Sipërfaqja (m²)
7	7512475.777	4691657.641	611.643	garazha	Përdhesa	Përdhesa	121.24
8	7512478.443	4691655.982	611.643	garazha			
9	7512481.42	4691648.905	611.643	perdhese			
14	7512476.094	4691652.372	611.643	perdhese			
15	7512476.732	4691653.353	611.643	perdhese_terasa		Terasa 1	7.431
17	7512466.984	4691644.13	611.643	perdhese_terasa			
42	7512482.045	4691649.896	611.643	perdhese_terasa		Terasa 2	5.96
43	7512470.535	4691641.819	611.643	perdhese			
44	7512475.086	4691638.858	611.643	perdhese		Gjithsej:	134.63
46	7512467.752	4691645.31	611.643	perdhese			
55	7512471.3	4691643.001	611.643	perdhese			


Republika e Kosovës

Republika Kosova-Republic of Kosova


Qeveria -Vlada-Government

Ministria e Mjedisit dhe Planifikimit Hapësinor /Ministarstvo Sredine i Prostornog Planiranja/Ministry of Environment and Spatial Planning

AGJENCIA KADASTRALE E KOSOVËS/ KATASTARSKA AGENCIJA KOSOVA/ KOSOVA CADASTRAL AGENCY

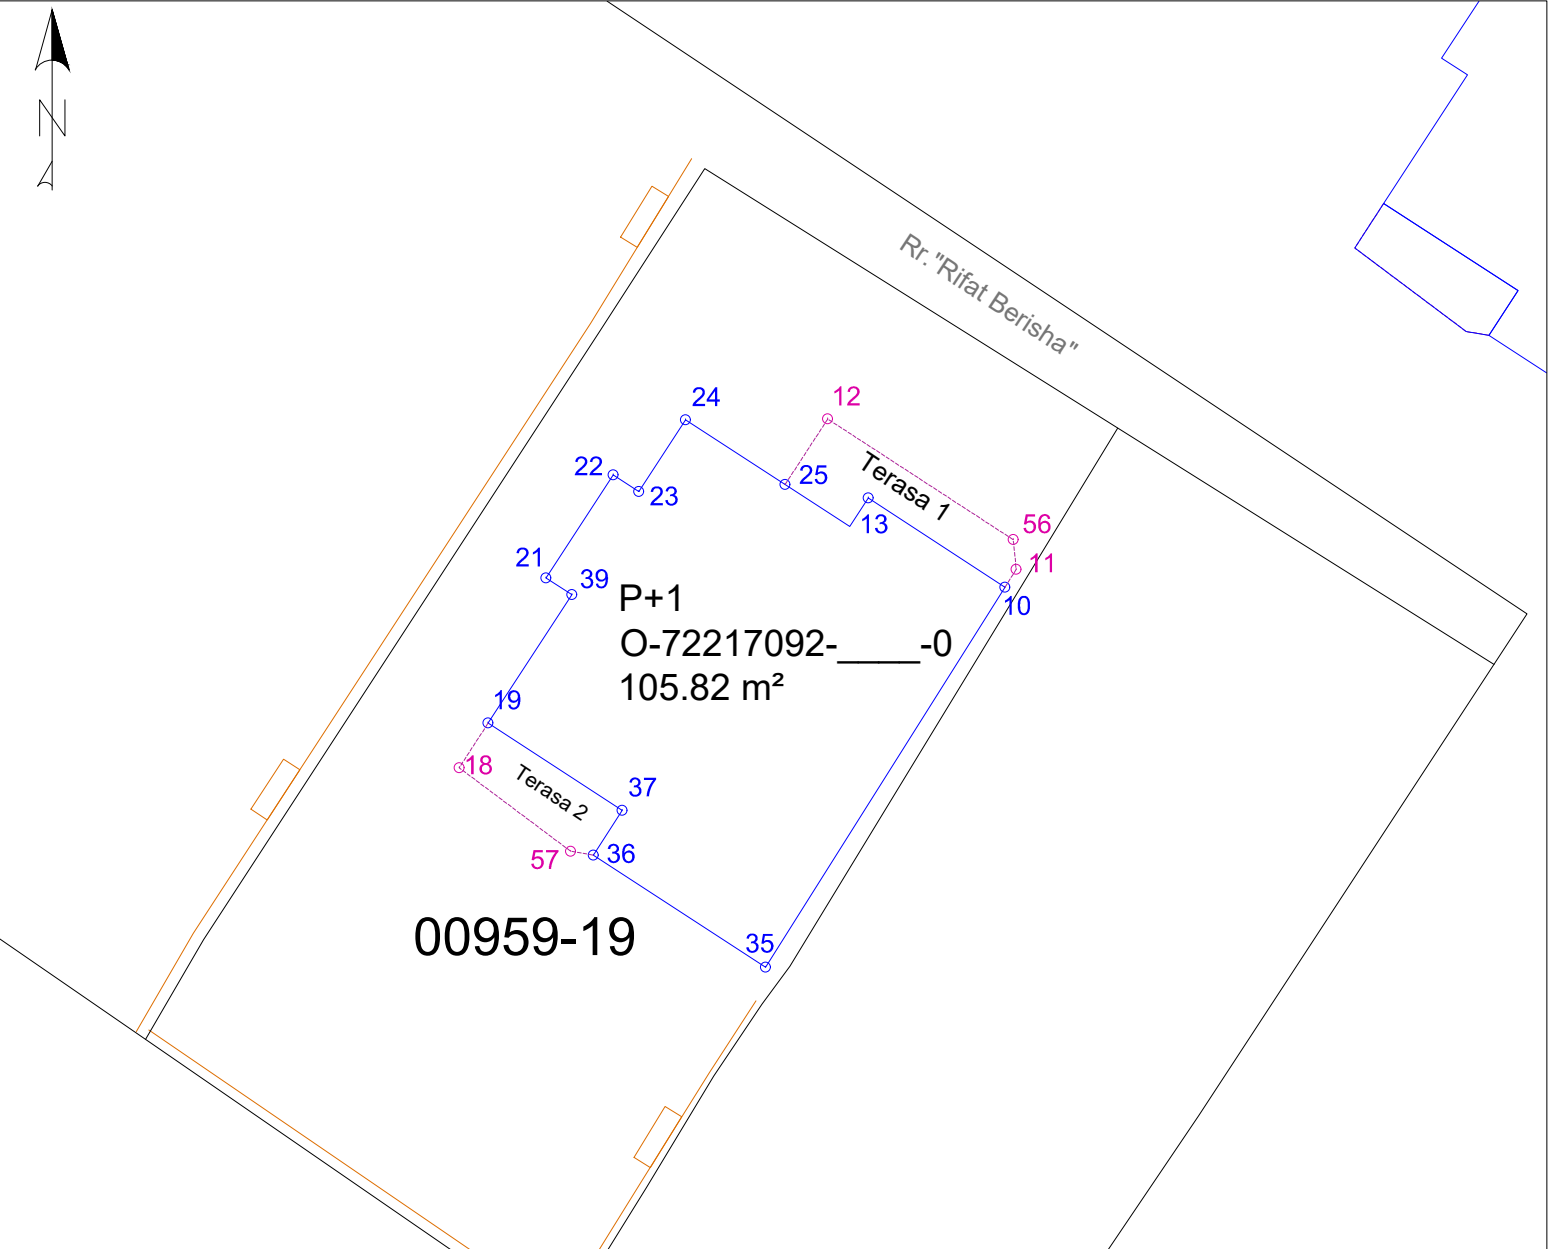

Nr.	Y	X	H	D	Etazhi	Sqarim	Sipërfaqja (m²)
10	7512481.42	4691648.91	614.37	kati1	Kati 1	Kati 1	105.82
13	7512477.80	4691651.26	614.37	kati1			
19	7512467.75	4691645.31	614.37	kati1			
21	7512469.28	4691649.15	614.37	kati1			
22	7512471.06	4691651.87	614.37	kati1			
23	7512471.74	4691651.43	614.37	kati1			
24	7512472.97	4691653.33	614.37	kati1		Terasa 1	9.11
25	7512475.61	4691651.62	614.37	kati1			
35	7512475.09	4691638.86	614.37	kati1			
36	7512470.53	4691641.82	614.37	kati1		Terasa2	6.48
37	7512471.30	4691643.00	614.37	kati1			
39	7512469.96	4691648.71	614.37	kati1			
11	7512481.72	4691649.38	614.37	kati1-terasa		Gjithsej:	121.40
12	7512476.73	4691653.35	614.37	kati1-terasa			
18	7512466.98	4691644.13	614.37	kati1-terasa			
56	7512481.64	4691650.16	614.37	kati1_terasa			
57	7512469.93	4691641.92	614.37	kati1_terasa			

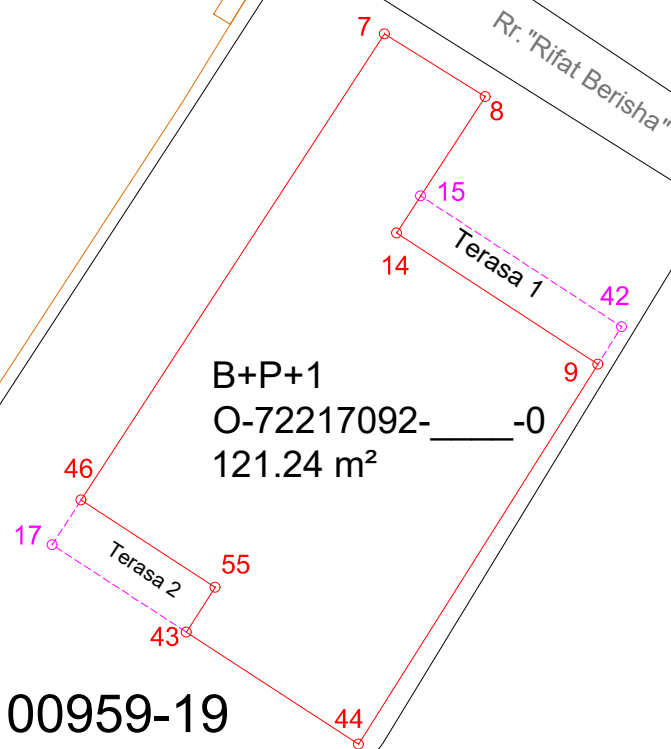

Nr	Y	X	H	Kodi	Përshkrimi	Burimi
7	7512475.777	4691657.641	611.643	40	Shtëpi-Ndërtesë	PM
8	7512478.443	4691655.982	611.643	40	Shtëpi-Ndërtesë	PM
9	7512481.420	4691648.905	611.643	40	Shtëpi-Ndërtesë	PM
14	7512476.094	4691652.372	611.643	40	Shtëpi-Ndërtesë	PM
43	7512470.535	4691641.819	611.643	40	Shtëpi-Ndërtesë	PM
44	7512475.086	4691638.858	611.643	40	Shtëpi-Ndërtesë	PM
46	7512467.752	4691645.310	611.643	40	Shtëpi-Ndërtesë	PM
55	7512471.300	4691643.001	611.643	40	Shtëpi-Ndërtesë	PM

Rilevoi / Snimio: LIRIDON SEJDIU
(emri dhe mbiemri i gjeodetit/kompanisë/ ime i prezime geodeta/ kompanije)

Aprovoi / Usvojio: _____
(emri dhe mbiemri i përsônit zyrtar/ ime i prezime sluzbenog lica)

Nr. i licencēs / Br. licence: 140

V.V.

Nënshkrimi / Potpis:

Nënshkrimi / Potpis: _____

Data e rilevimit / Datum snimanja: 31.10.2025

Data e rilevimit / Datum snimanja:



Republika e Kosovës
Republika Kosova - Republic of Kosovo
Qeveria e Kosovës - Vlada Kosova - Government of Kosovo
Ministria e Infrastrukturës dhe Ambientit/ Ministrastvo Infrastrukture i Sredine/ Ministry of Infrastructure and Environment
AGJENCIA KADASTRALE E KOSOVËS/ KOSOVSKA KATASTARSKA AGENCIJA/ KOSOVA CADASTRAL AGENCY

R E G J I S T R I M I I N D E R T E S Ë S / S H T Ë P I S Ë													
Nr	Komuna	Zona Kadastrale	Numri i ndërtesës (njësia)	Etazhiteti	Katet	Sipërfaqja e kateve [m²]	Sipërfaqja e bazamentit [m²]	Adresa e Njesisë	Vendi i quajtur	Shfrytëzimi i aktual	Pronari / Shfrytëzuesi Emri (Emri i prindit) Mbiemri	Numri personal	Pjesa e Pronës
1	Ferizaj	Ferizaj	O-72217092-0959-19____-0	B+P+1	Bodrumi	103.92	121.24	Rr. "Rifat Berisha" - Ferizaj	ARAT E TJEGULLAVE	Banim	VIOLETA MEHMETI (SHEFKI)	2011639367	1/1
					Përdhesa	121.24							
					Kati 1	105.82							
					Gjithsej:	330.98							

Gjeodeti/kompania e licencuar: LIRIDON SEJDIU	Nr i licencës: 140	Nënshkrimi dhe vula:
---	--------------------	----------------------



Republika e Kosovës
Republika Kosova-Republic of Kosovo
Qeveria e Kosovës- Vlada Kosova- Government of Kosovo
Ministria e Infrastrukturës dhe Ambientit/ Ministrastvo Infrastrukture i Sredine/ Ministry of Infrastructure and Environment
AGJENCIA KADASTRALE E KOSOVËS/KOSOVSKA KATASTARSKA AGENCIJA/ KOSOVO CADASTRAL AGENCY

Komuna: Ferizaj	Zona Kadastrale: Ferizaj
Numri i njësis kadastrale: 00959-19	Sistemi koordinat: KosovaRef01

Nr	Y	X	H	Kodi	Përshkrimi	Burimi
7	7512475.777	4691657.641	611.643	40	Shtëpi-Ndërtesë	PM
8	7512478.443	4691655.982	611.643	40	Shtëpi-Ndërtesë	PM
9	7512481.420	4691648.905	611.643	40	Shtëpi-Ndërtesë	PM
14	7512476.094	4691652.372	611.643	40	Shtëpi-Ndërtesë	PM
43	7512470.535	4691641.819	611.643	40	Shtëpi-Ndërtesë	PM
44	7512475.086	4691638.858	611.643	40	Shtëpi-Ndërtesë	PM
46	7512467.752	4691645.310	611.643	40	Shtëpi-Ndërtesë	PM
55	7512471.300	4691643.001	611.643	40	Shtëpi-Ndërtesë	PM

Gjeodeti / Kompania gjeodete e licencuar:	Liridon Sejdiu	Nënshkrimi dhe vula:	
Numri i licencës	140		



Republika e Kosovës
Republika Kosova-Republic of Kosovo
Qeveria - Vlada - Government
Ministria e Mjedisit, Planifikimit Hapësinor dhe Infrastrukturës / Ministarstvo Životne Sredine, Prostornog Planiranja i Infrastrukture /
Ministry of Environment, Spatial Planning and Infrastructure
AGJENCIA KADASTRALE E KOSOVËS / KATASTARSKA AGENCIJA KOSOVA / KOSOVO CADASTRAL AGENCY

CERTIFIKATË / CERTIFIKAT / CERTIFICATE

NJËSIA KADASTRALE / KATASTARSKA JEDINICA / CADASTRAL UNIT : P-72217092-00959-19

Numri i lëndës / Broj Predmet / Case Referent Number:	Certificate draft
Data dhe koha e lëshimit / Datum i vreme izdavanja / Date and time of submission:	31.10.2025 - 08:44
Komuna / Opština / Municipality:	FERIZAJ / UROŠEVAC / FERIZAJ
Zona kadastrale / Katastarska Zona / Cadastral Zone:	Ferizaj / Uroševac / Ferizaj
Zyra Kadastrale Komune / Opštinska Katastarska Kancelarija / Municipal Cadastral Office:	FERIZAJ / UROŠEVAC / FERIZAJ

A. TË DHËNAT PËR NJËSINË KADASTRALE / PODACI O KATASTARSKOJ JEDINICI / CADASTRAL UNIT DATA

Numri i njësise kadastrale Broj katastarske jedinice Cad. Unit. No.	Lloji i njësise Vrsta Jedinice Unit Type	Lloji i pronës Vrsta imovine Property Type	Zona U/R G/S U/R	Sipërfaqja Površina Area (m²)	Përshkrim Opis Description	Krijuar më datën Uradjeno na dan Created On	Azhuruar Ažurirano Updated
P-72217092-00959-19	PARCELË / PARCELA / PARCEL	Pronë private / Privatna imovina / Privately owned Land	Urban	365	136/2024 rfp	15.08.2024	

A.1 ADRESA E NJËSISË KADASTRALE / ADRESA KATASTARSKE JEDINICE / CADASTRAL UNIT ADDRESS

Vendi i quajtur Mesto zvano Called place	Kodi Postal Poštanski Kod Postal Code	Emri i rrugës Naziv ulice Street name	Azhuruar Ažurirano Updated
ARAT E TJEGULLAVE			15.08.2024

A.2 LLOJI I SHFRYTËZIMIT / VRSTA KORISCENJA / TYPE OF USE

Numri Broj Number	Lloji i shfrytëzimit të parcelës Vrsta koriscenja parcele Parcel Type Of Use	Shfrytëzimi aktual i parcelës Trenutno koriscenje parcele Parcel Current Use	Kualiteti i klasës Kvalitet klase Quality Class	Sipërfaqja Površina Area (m²)
1	Bujqësore/Poljoprivredno/Agriculture	Ara/Njive/Arable Land	Arë E Klasës I/Njiva 1 Klase/1st Class Arable Land	365

B. PRONARI/POSEDUESI - VLASNIK/DRŽALAC - OWNER/POSSESSOR

Të drejtat Prava Rights	Emri Ime Name	Nr. personal Licni broj ID. No.	Vendbanimi Prebivaliste Resident	Kodi postal Poštanski kod Postal code	Hollësitë e adresës Pojednosti adrese Address details	Pjesa e pronës Deo imovine Share quota	Pershkrimi Opis Description	Azhuruar Azurirano Updated
Posedim individual / Individualna Drzavina / Single possessor	Mehmeti Violeta (Shefki)	2011639367	FERIZAJ / UROŠEVAC / FERIZAJ /		Rruga/Hivzi Sylejmani"P.n.r.	1/1	400/2024 - Ndarje fizike LRP nr.27469/2024, Nr.ref.9178/2024	03.10.2024







42

05 • 805 • FF







